


FACADE GLASS PARTITION

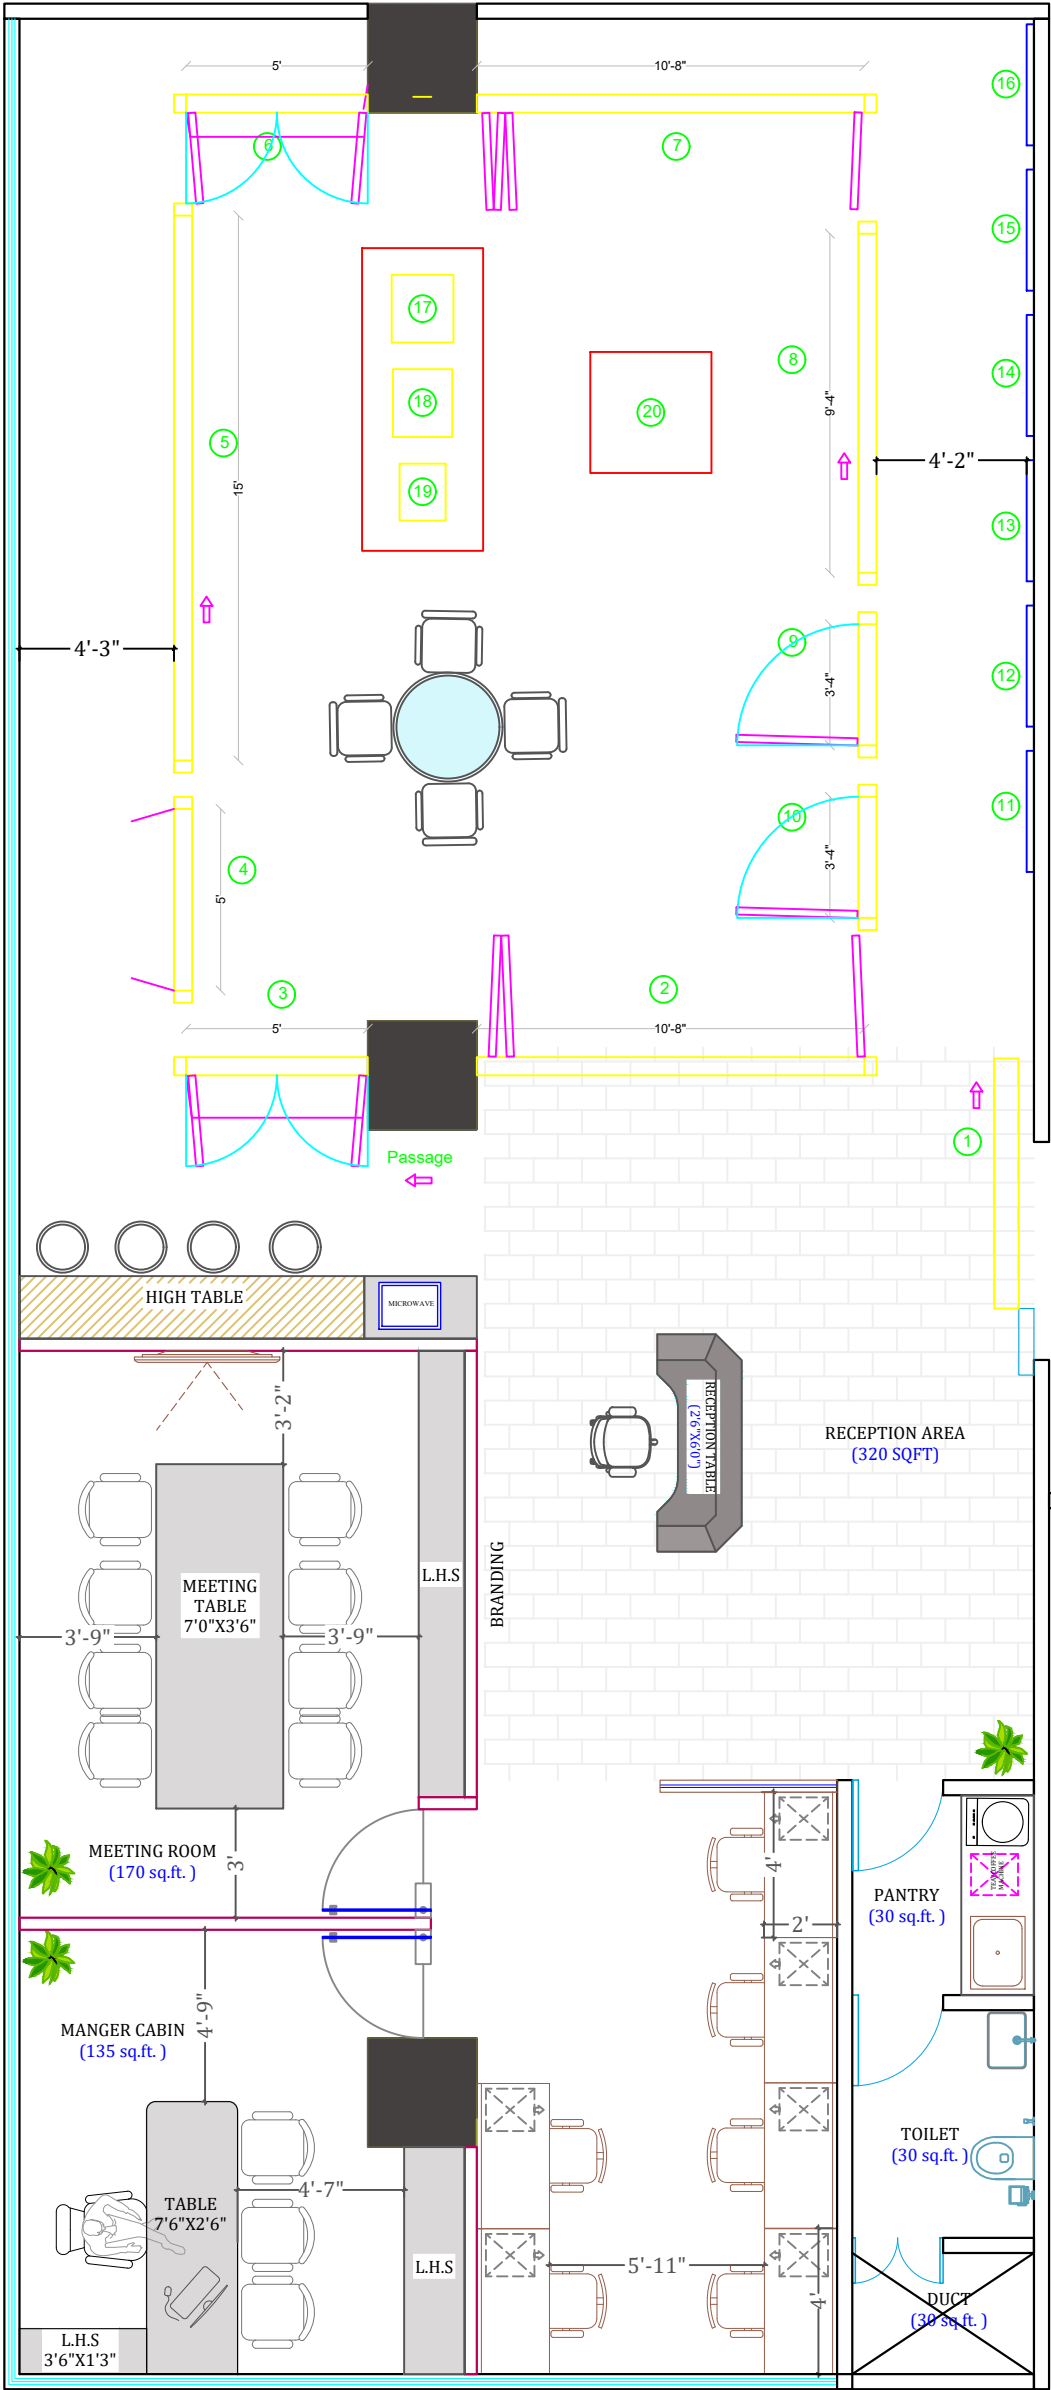

ENTRANCE

OPTION-04

9' - 0" W I D E P A S S A G E

TITLE :		
INTERIOR LAYOUT		
LEGEND :		
GYPSUM FULL HT. PARTITION		
GLASS PARTITION		
SIPOREX WALL		
L.H.S - LOW HT. STORAGE		
F.H.S - FULL HT. STORAGE		
A C D - ACCESS CONTROL DOOR		
SR. NO.	ITEMS	REQ
1.	RECEPTION AREA	1
2.	SEATING AREA	1
3.	WORK STATIONS (4'-0" x 2'-0")	6
4.	MEETING ROOM - 8 SEATS	1
5.	CABINS CABIN	1
6.	TOILET	1
7.	PANTRY	1
This drawing is the property of "JASFO DESIGN PVT. LTD." and is not to be reproduced or copied.		
CLIENT :		
G U		
ARCHITECT :		
JASFO DESIGN		
DRAWN BY : ZOYEB JAMADAR		
CHECKED BY :		
DWG. NO.	ORIENTATION	
6	W E S	
REV. NO.		
-		
ISSUE DATE	SCALE	
12-06-2026	NTS	